План першого поверху
М(1:75)

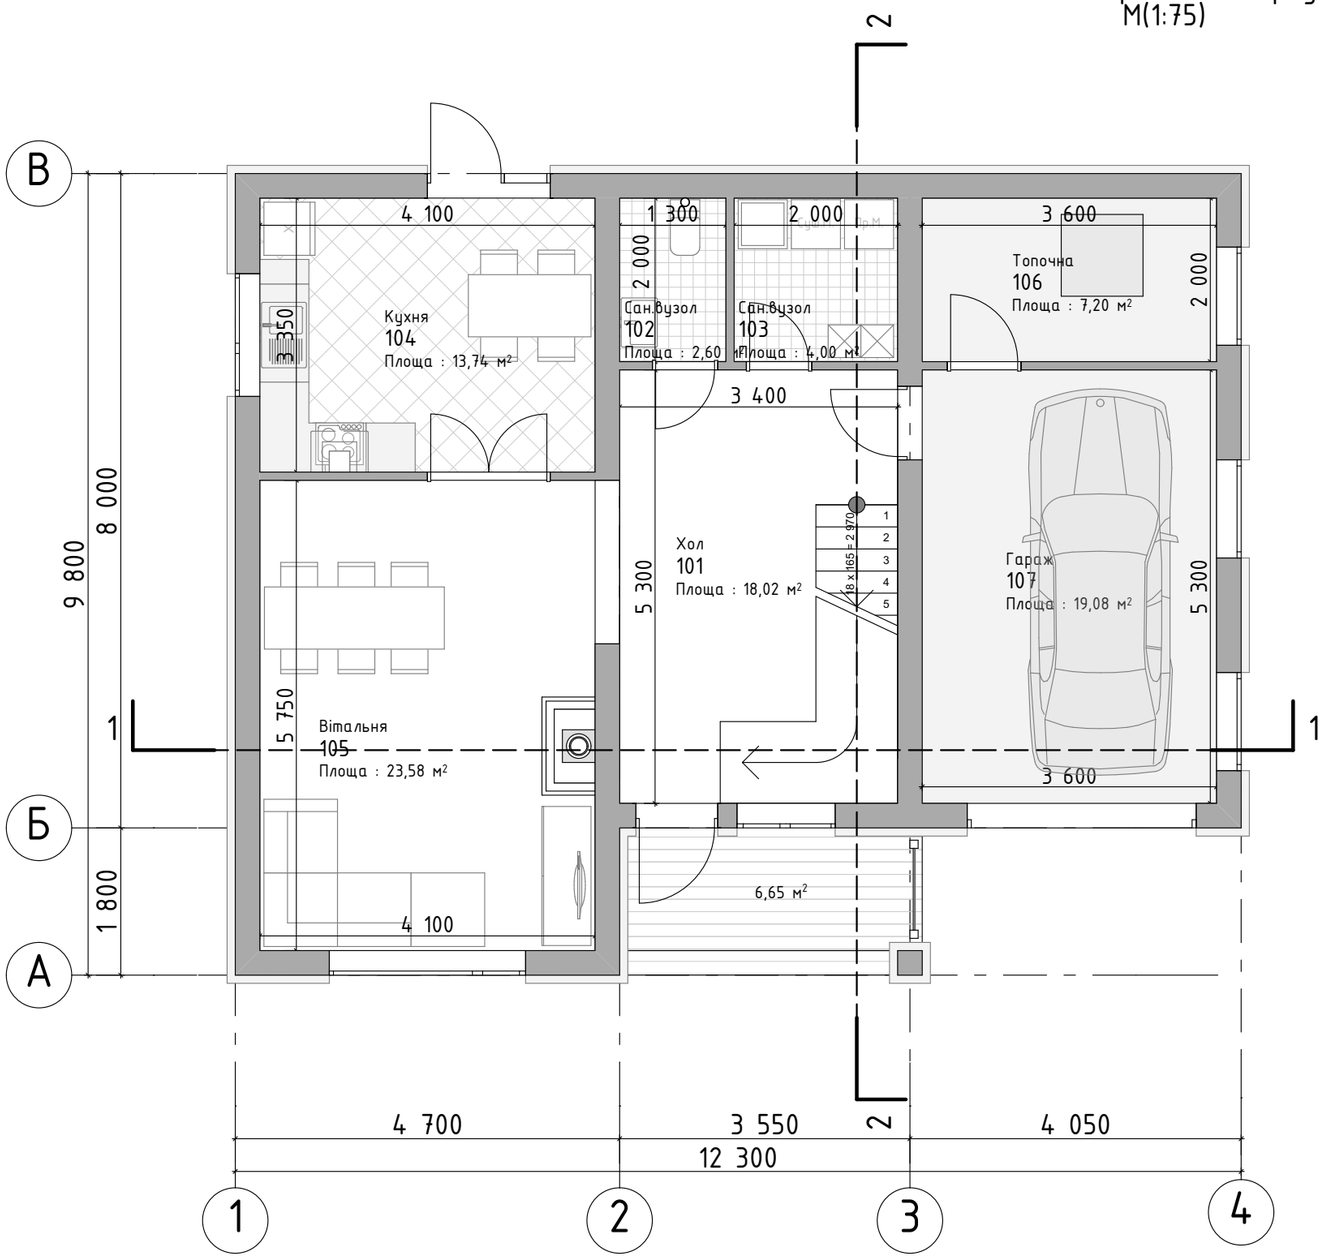

Експлікація приміщень першого поверху

№	Найменування	Площа
101	Хол	18,02
102	Сан.вузол	2,60
103	Сан.вузол	4,00
104	Кухня	13,74
105	Вітальня	23,58
106	Топочна	7,20
107	Гараж	19,08
	Загальна площа поверху	88,22 м²
	Загальна площа будинку	172,46 м²

Зм.	Кіл.	Лист	№док.	Підп.	Дата	№ ПКЕ13/07-2021			
						Проект індивідуального житлового будинку за адресою: Київська область, м. Вишневе, вул. Григорія Сковороди, 27-д. Кадастровий номер ділянки: 3222410600:01:015:5447			
						Індивідуальний житловий будинок	Стадія	Аркуш	Аркушів
							ЕП	АБ.1	
Виконав						План першого поверху М(1:75)	EURO HOUSE DREAM FAMILY HOUSE		
Перевірив									

План другого поверху
М(1:75)

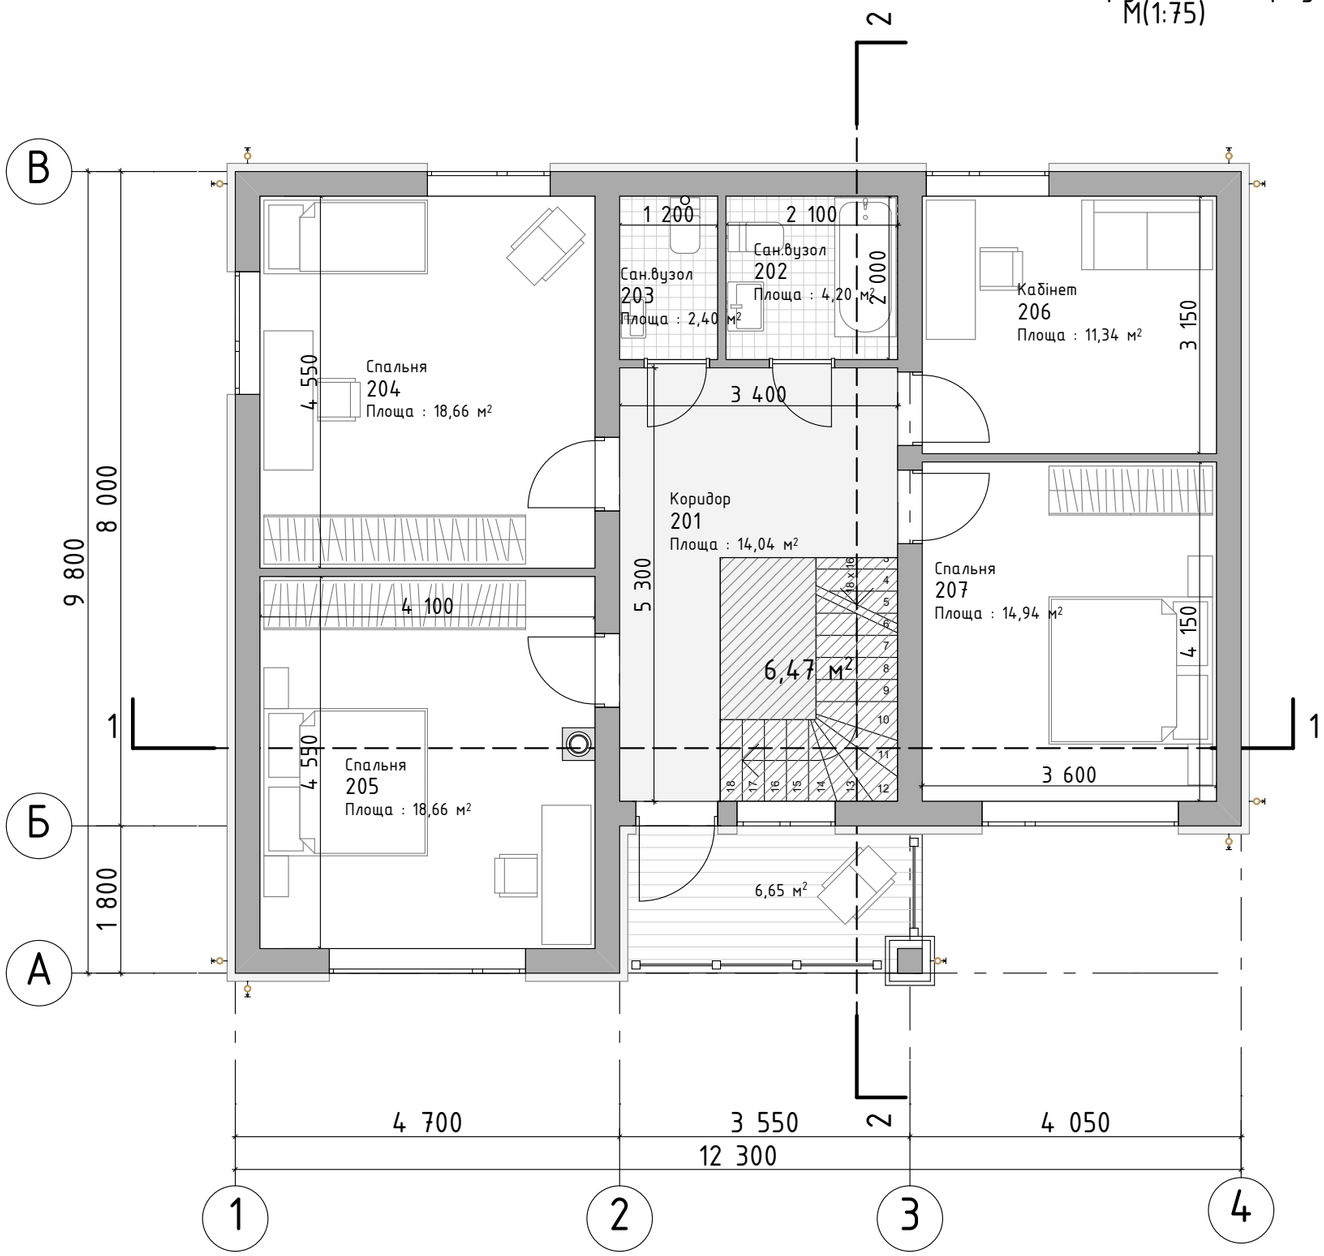

Експлікація приміщень другого поверху

№	Найменування	Площа
201	Коридор	14,04
202	Сан.вузол	4,20
203	Сан.вузол	2,40
204	Спальня	18,66
205	Спальня	18,66
206	Кабінет	11,34
207	Спальня	14,94
	Загальна площа поверху	84,24 м²
	Загальна площа будинку	172,46 м²

Зм.	Кіл.	Лист	№док.	Підп.	Дата
Виконав					
Перевірив					

№ ПКЕ13/07-2021

Проект індивідуального житлового будинку за адресою:
Київська область, м. Вишневе, вул. Григорія Сковороди, 27-д.
Кадастровий номер ділянки: 3222410600:01:015:5447

Індивідуальний житловий будинок

Стадія	Аркуш	Аркушів
ЕП	АБ.2	

План другого поверху
М(1:75)

EURO HOUSE
DREAM FAMILY HOUSE

Фасад 1-4
М(1:75)

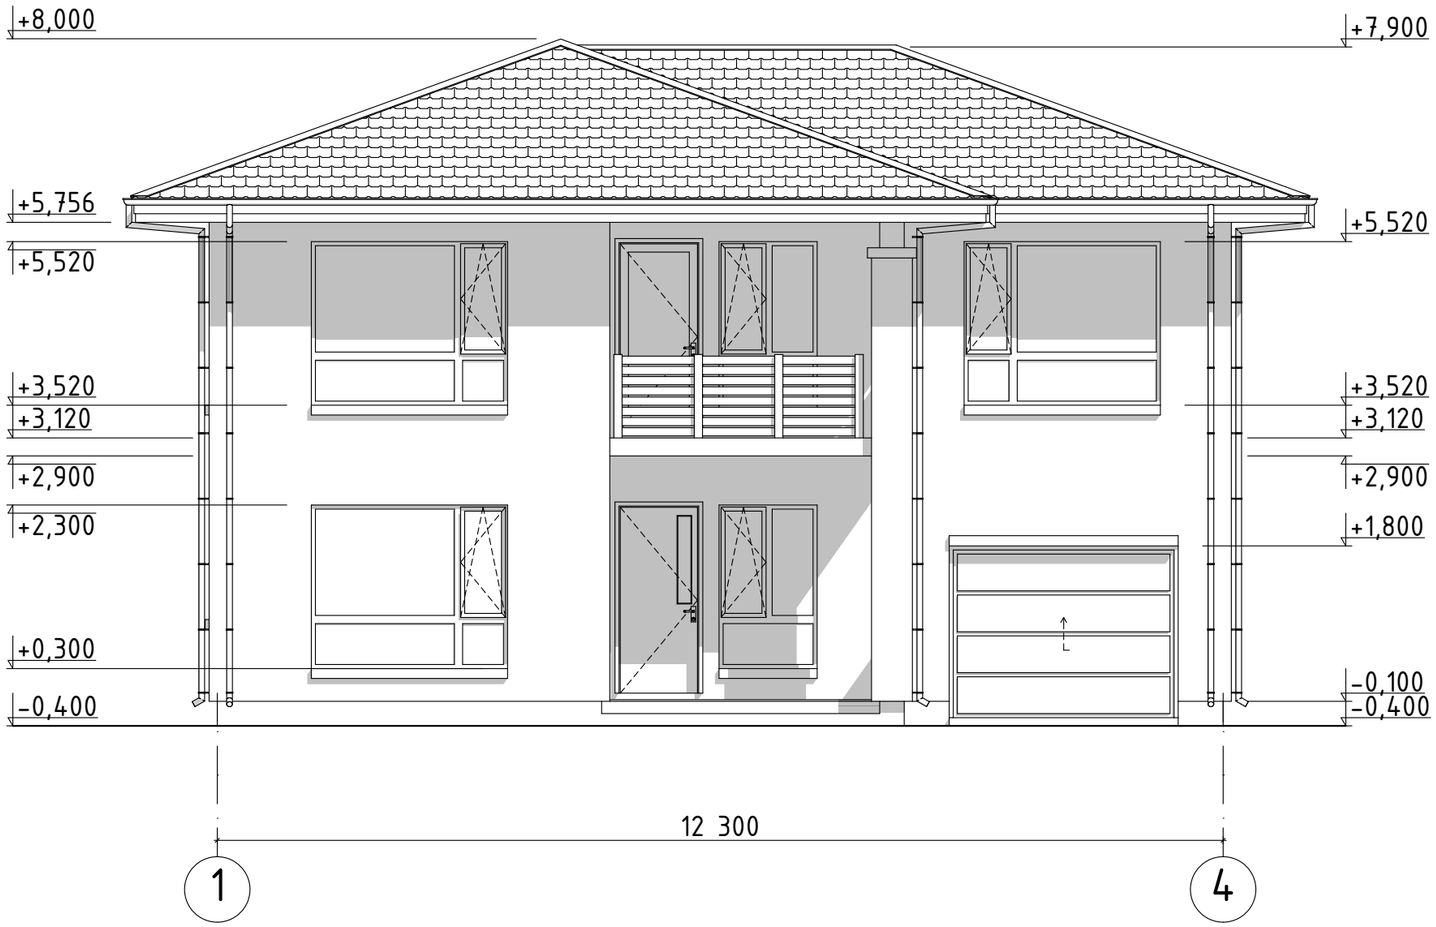

						№ ПКЕ13/07-2021
						Проект індивідуального житлового будинку за адресою: Київська область, м. Вишневе, вул. Григорія Сковороди, 27-д. Кадастровий номер ділянки: 3222410600:01:015:5447
Зм.	Кіл.	Лист	№док.	Підп.	Дата	
						Індивідуальний житловий будинок — Стадія: ЕП; Аркуш: АБ.3; Аркушів:
Виконав						Фасад 1-4 М(1:75)
Перевірив						EURO HOUSE DREAM FAMILY HOUSE

Фасад 4-1
М(1:75)

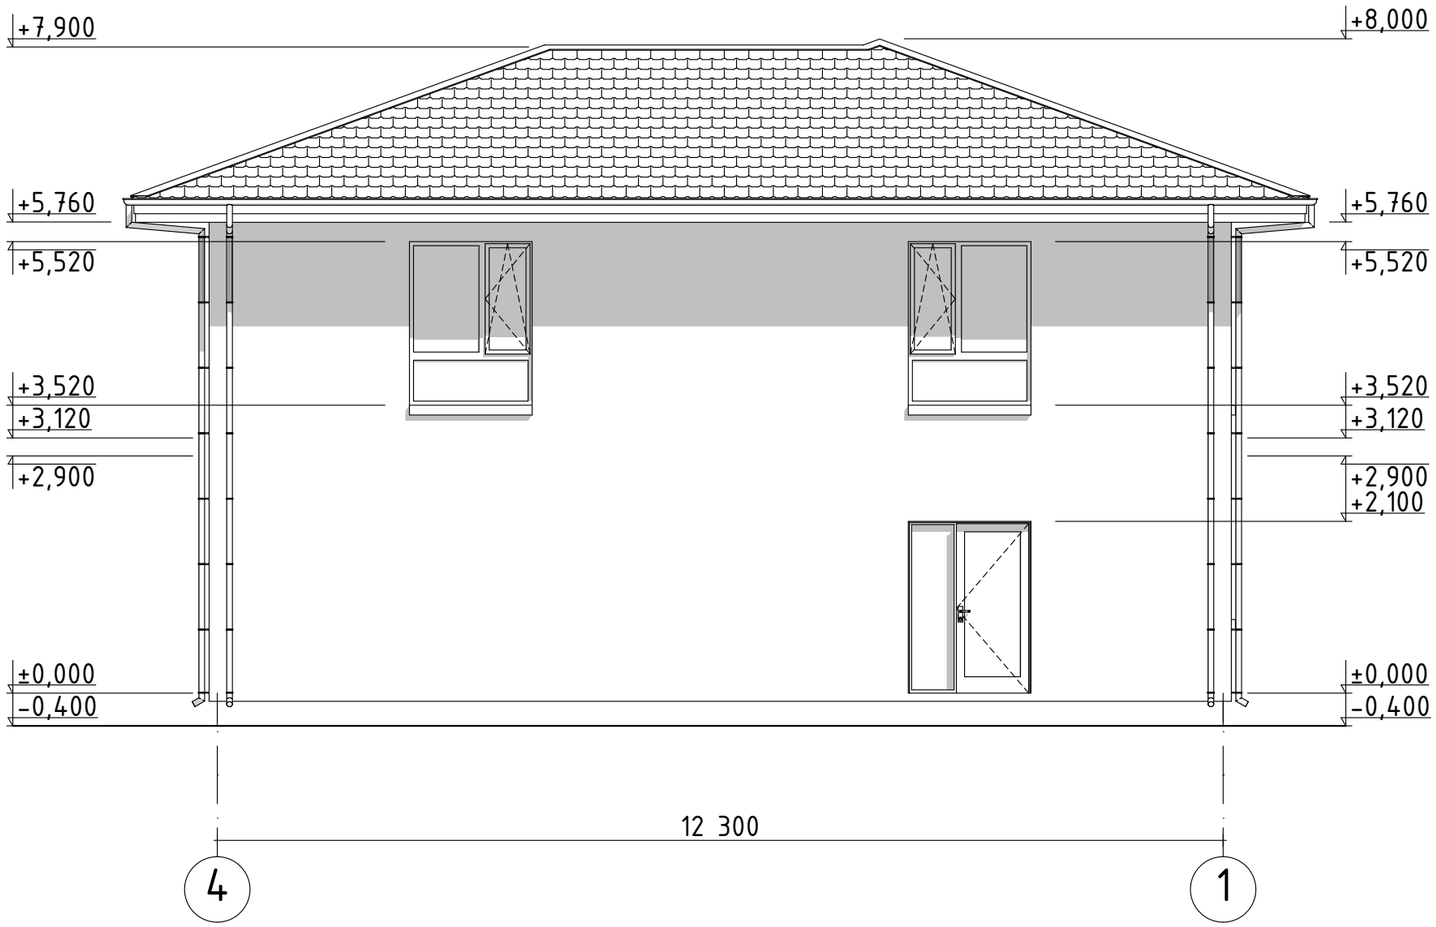

						№ ПКЕ13/07-2021
						Проект індивідуального житлового будинку за адресою: Київська область, м. Вишневе, вул. Григорія Сковороди, 27-д. Кадастровий номер ділянки: 3222410600:01:015:5447
Зм.	Кіл.	Лист	№док.	Підп.	Дата	
						Індивідуальний житловий будинок — Стадія: ЕП; Аркуш: АБ.4; Аркушів:
Виконав						Фасад 4-1 М(1:75)
Перевірив						EURO HOUSE DREAM FAMILY HOUSE

Фасад А-В
М(1:75)

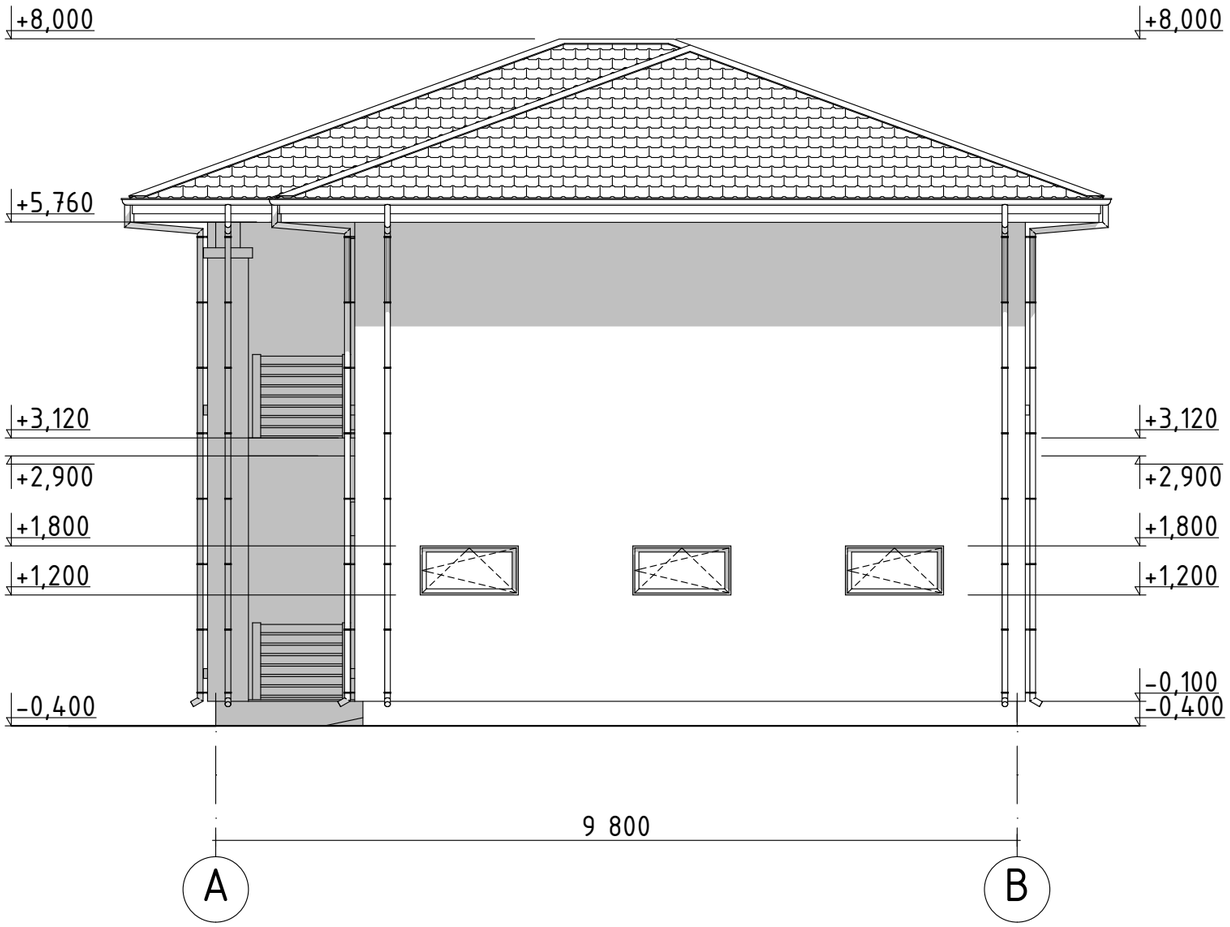

Зм.	Кіл.	Лист	№док.	Підп.	Дата	№ ПКЕ13/07-2021
						Проект індивідуального житлового будинку за адресою: Київська область, м. Вишневе, вул. Григорія Сковороди, 27-д. Кадастровий номер ділянки: 3222410600:01:015:5447
						Індивідуальний житловий будинок — Стадія: ЕП; Аркуш: АБ.5; Аркушів:
Виконав						Фасад А-Г М(1:75)
Перевірив						EURO HOUSE DREAM FAMILY HOUSE

Фасад В-А
М(1:75)

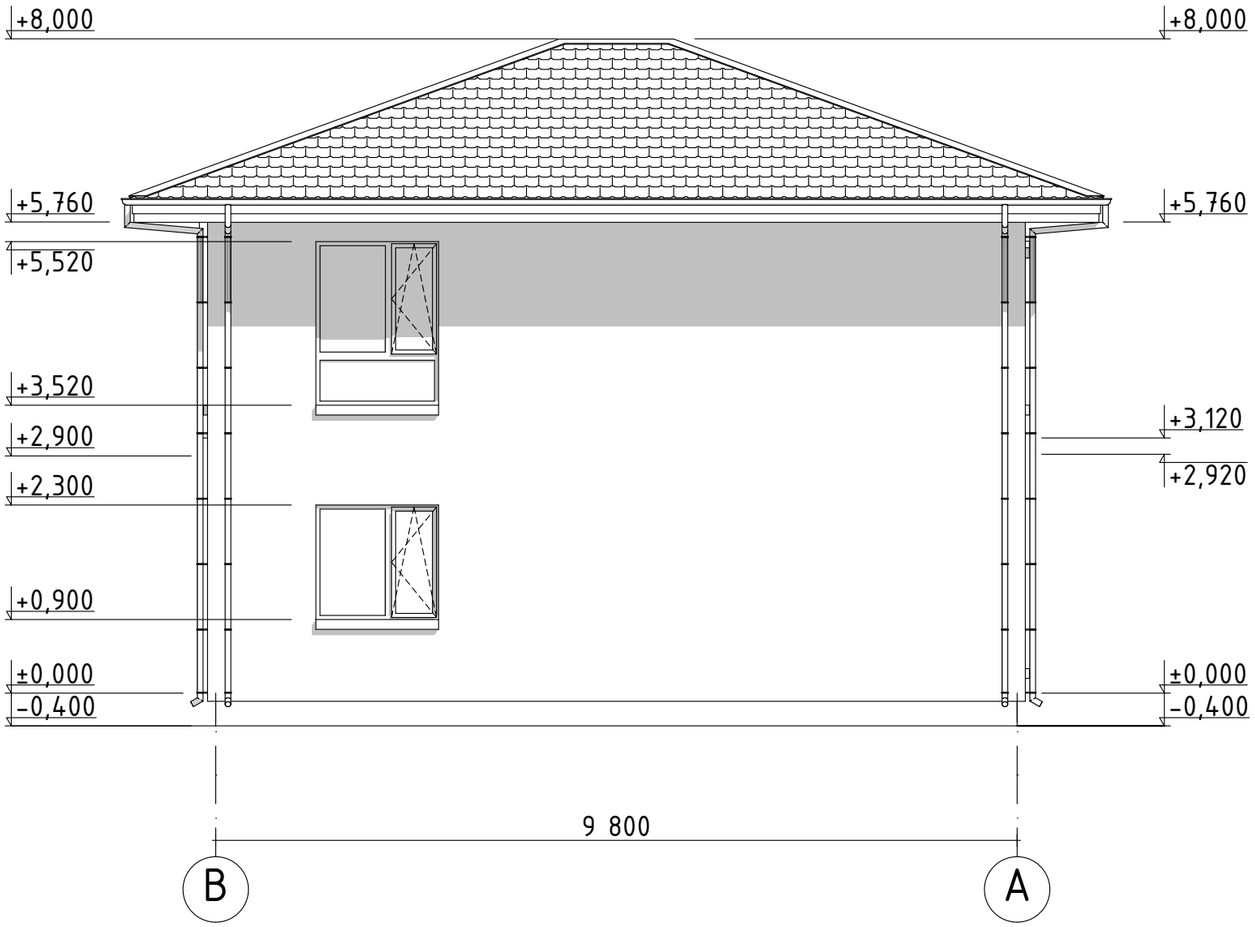

						№ ПКЕ13/07-2021		
						Проект індивідуального житлового будинку за адресою: Київська область, м. Вишневе, вул. Григорія Сковороди, 27-д. Кадастровий номер ділянки: 3222410600:01:015:5447		
Зм.	Кіл.	Лист	№док.	Підп.	Дата			
						Індивідуальний житловий будинок	Стадія	Аркуш	Аркушів
							ЕП	АБ.6	
Виконав						Фасад Г-А М(1:75)	EURO HOUSE DREAM FAMILY HOUSE		
Перевірив									